
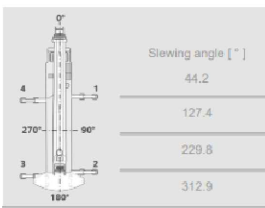


ATF 70G-4 EU Stage IV (52,1m) (Standard)
Boom without Jib

CONFIGURATION			
Jib - Configuration [m]	0	Slewing angle	Maximum ground bearing load in service in working area
Jib - Adjustment angle [°]	0	Hook block [t Lifting load]	Included in load
Boom length [m]	52.1 m	Weight of slings [t]	0 t
Boom extension sequence [%]	100-100-100-100-100	Working radius [m]	25.0 m
Counterweight [t]	16.5 t	Boom angle [°]	64.0 °
Outrigger base [m]	6.4 m	Lifting load [t]	1.29 t
Number of ropes 1			
Usable rope length [m] 157.90 m			
Underfloor height [m] -112.8 m			
Center of gravity X (to slewing center [m]) -			
Center of gravity Y (to slewing center [m]) -			

GROUND FORCES [t]					
	Outrigger				
		1	2	3	4
	Slewing angle [°]				
	44.2	17	15	9	10
	127.4	11	22	12	6
229.8	6	12	22	11	
312.9	10	9	15	17	

Maximum ground bearing load in service in working area

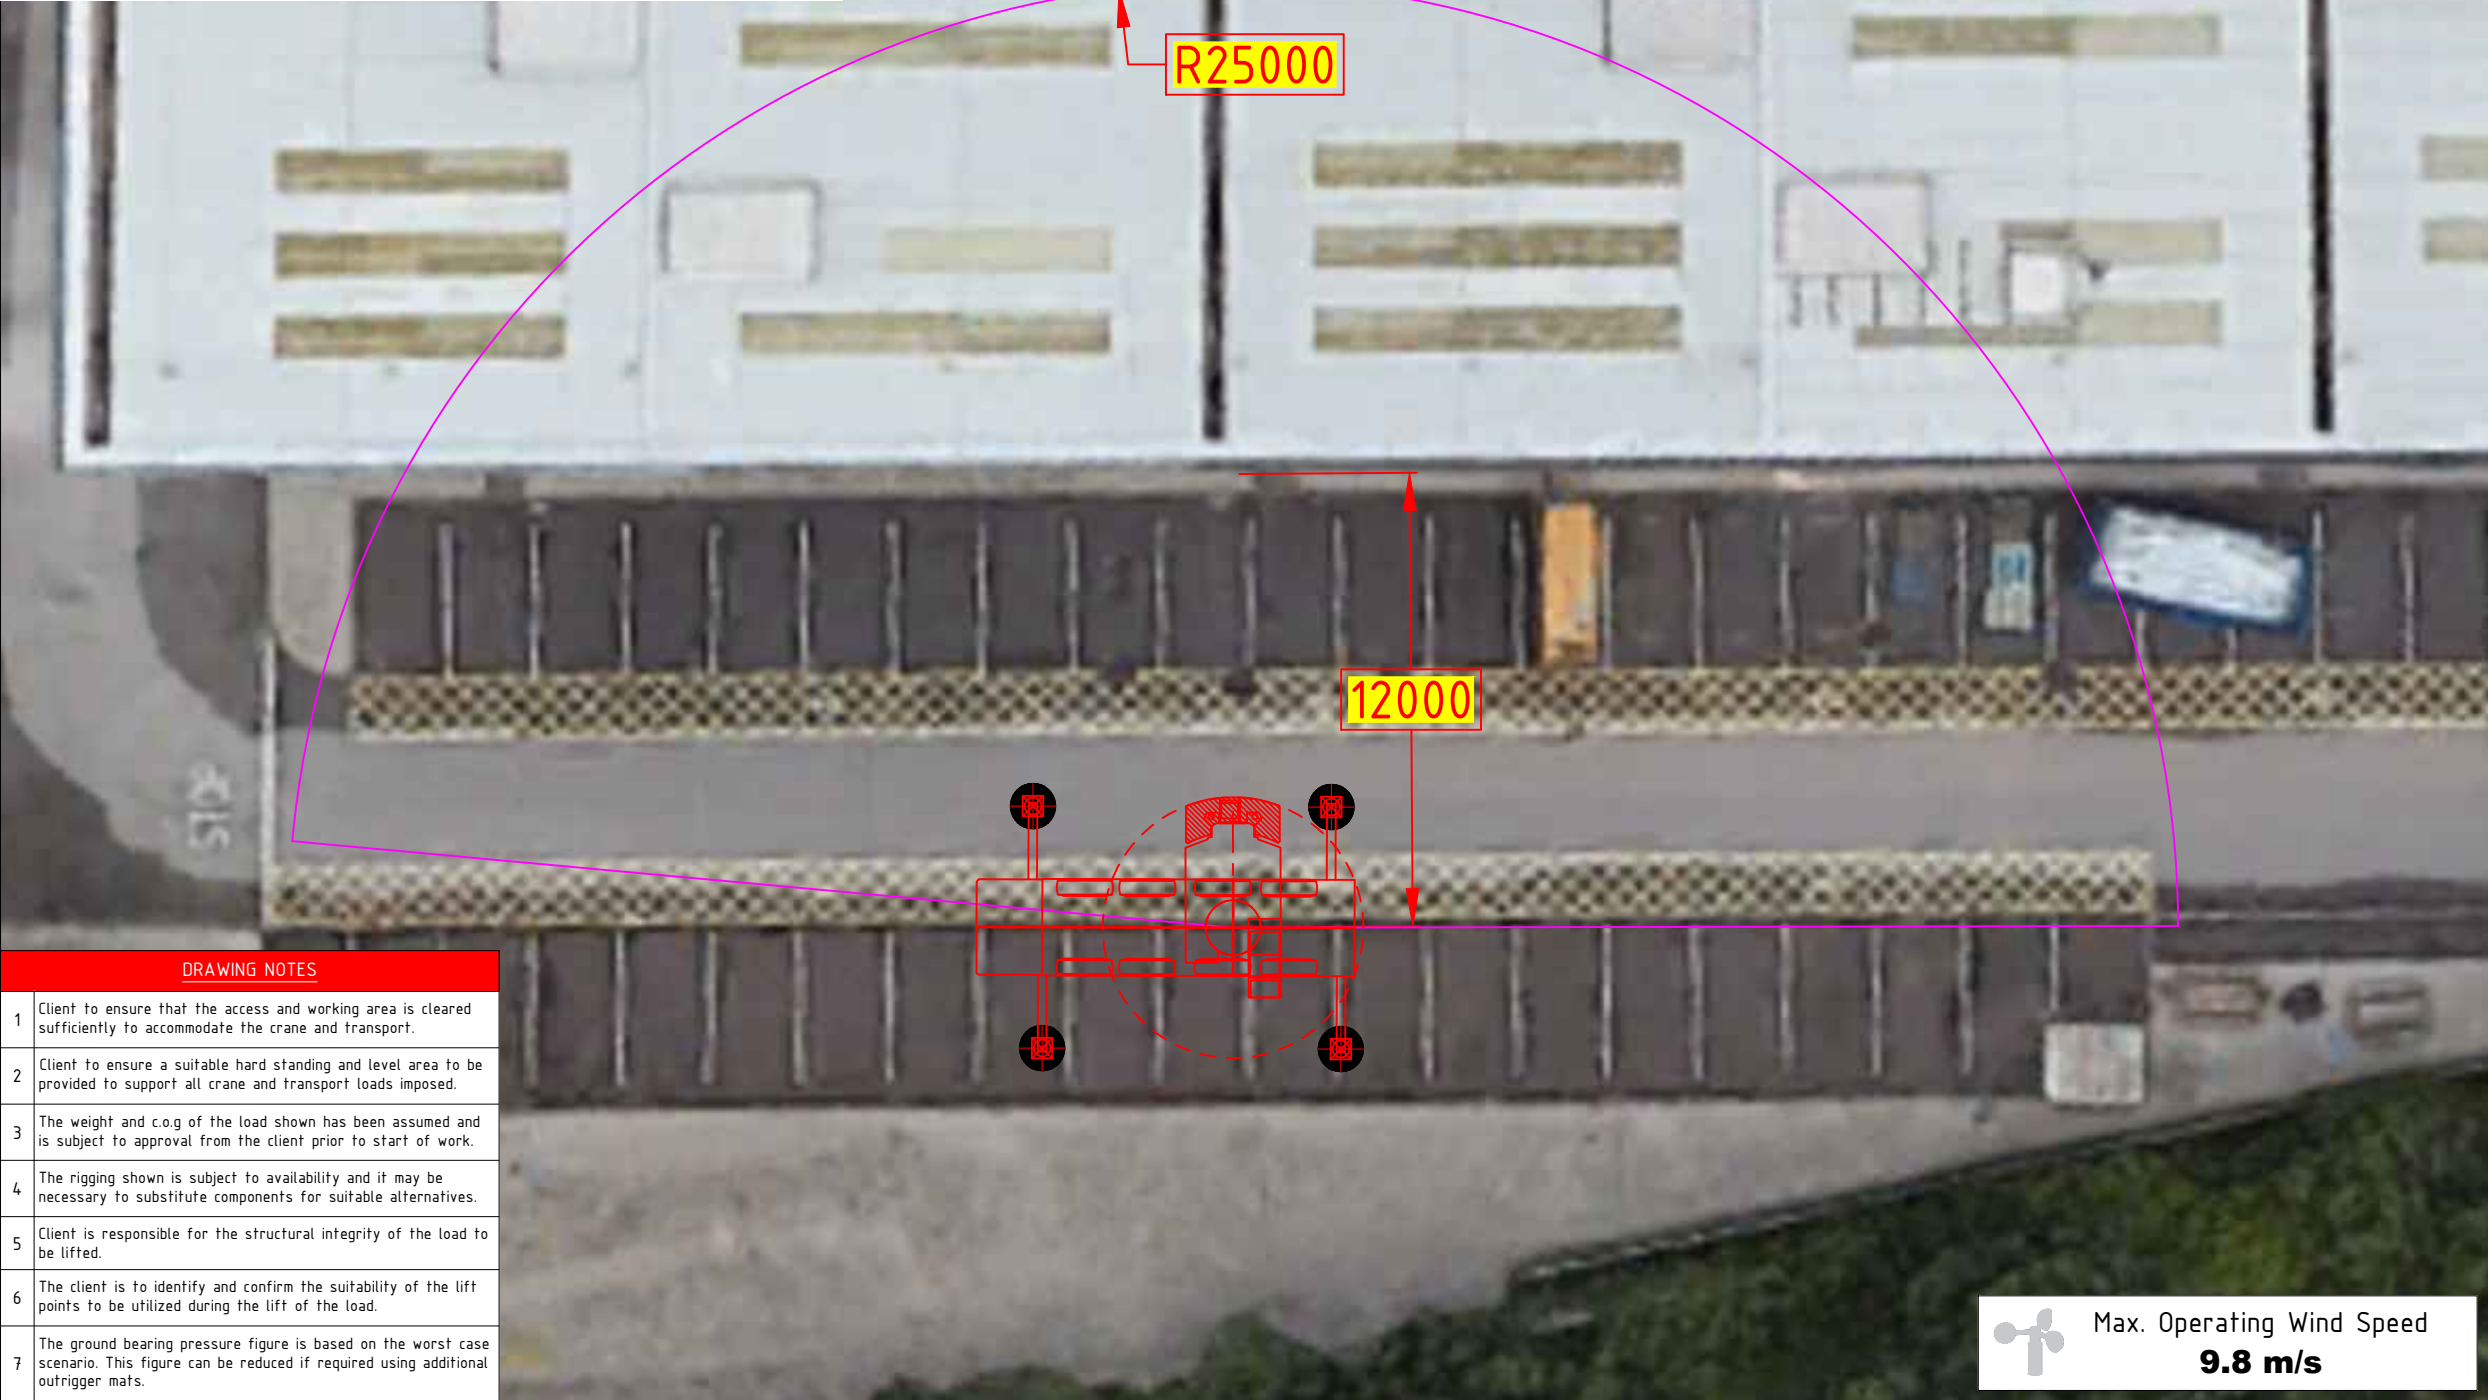

DRAWING NOTES

- Client to ensure that the access and working area is cleared sufficiently to accommodate the crane and transport.
- Client to ensure a suitable hard standing and level area to be provided to support all crane and transport loads imposed.
- The weight and c.o.g of the load shown has been assumed and is subject to approval from the client prior to start of work.
- The rigging shown is subject to availability and it may be necessary to substitute components for suitable alternatives.
- Client is responsible for the structural integrity of the load to be lifted.
- The client is to identify and confirm the suitability of the lift points to be utilized during the lift of the load.
- The ground bearing pressure figure is based on the worst case scenario. This figure can be reduced if required using additional outrigger mats.

MAIN CRANE DATA (DIN ISO 75%)

Crane Model:	Tadano ATF70G-4L	
Lifting Configuration:	HA	
Outrigger Base Centres:	7.9 x 6.4	m
Counterweight:	16.50	te
Main Boom Length: (x.x°)	52	m
Telescopic Sections:	100-100-100-100-100	%
Hookblock Type: (SWL)	13.2	te
Outrigger Mats:	1.2	m
Additional Mats:	X	m

LIFT DETAILS – CRITICAL LIFT

Item To Be Lifted:	Roof Sheets	
Radius:	25.00	m
Item Weight:	1.00	te
Lifting Tackle:	0.10	te
Hookblock:	0.19	te
Total Lift Weight:	1.29	te
Gross Capacity:	4.20	te
(%) Of Capacity:	30.60	%

OUTRIGGER LOAD / MAT INFORMATION

Max Outrigger Force:	22.00		te
Standard Mats: (Dia.)	1.20	AREA	= 1.13 m²
Additional Mats: (Additional)	1.00	x	0.00 = 0.00 m²
Max. G B P: (Dia.)	19.45		te/m²
Max. G B P: (Additional)	####		te/m²

This Drawing & the information contained therein is the property of City Lifting Ltd. & is lent on the condition that it will not be reproduced, copied or disclosed, directly or indirectly nor used for any purpose other than for that which it is specifically furnished.

Original Size A3 / Do Not Scale

Client: Weatherproofing

Site: Iron Mountain, Thamesmead

Project: Lifting materials to roof level

Scale: 1:200 @ A3

Status: ISSUE

Title: PLAN VIEW

CAD No: D230721SG1

Sheet No: 1 of 1

Rev: 0

File Location: C:\Users\SteveGoodey\OneDrive - City Lifting Ltd\2023\Weatherproofing\Thamesmead

City Lifting

MOBILE CRANES DIVISION

9 Juliette Way
Purfleet Industrial Park
Purfleet
Essex
RM15 4YD

Tel 01708 805 550
Fax 01708 805 558



Max. Operating Wind Speed
9.8 m/s